


NOTE:
These drawings shall be read in conjunction with all structural & other consultants drawings & specifications and with such other written instruction as may be issued during the course of the contract.
Any discrepancies shall be referred to the building designer for decision before proceeding with the work.
Figured dimensions to be taken in preference to scaling from drawings.
During construction the building shall be maintained in a stable condition & no part shall be overstressed.
All workmanship shall be in accordance with the requirements of the SAA codes & by-laws & ordinances of the relevant building authority.
Dimensions are in millimetres.
All dimensions and levels shall be checked by the builder prior to the commencement of the works.
All timber framing sizes & spans to be in accordance with SAA timber framing code AS 1684.
All bracing of roof & wall framing to satisfy wind speed design category in accordance with BCA & AS 4055 to engineers certification.
All reinforced concrete shall be in accordance with engineers details.
Builder/developer to maintain erosion control in accordance with the clean waters act 1970.
Termite treatments in accordance with AS 3660 & AS 3660 part 1.
Builder to verify location of all services & vegetation prior to commencement of works.
All opening sizes to be confirmed on site prior to ordering of windows & doors
All Structural Steel is to be protected against corrosion in accordance with Structural Engineers recommendations.
The Waterproofing of all work is the builders responsibility.
All building work must be carried out in accordance with the Building Code of Australia

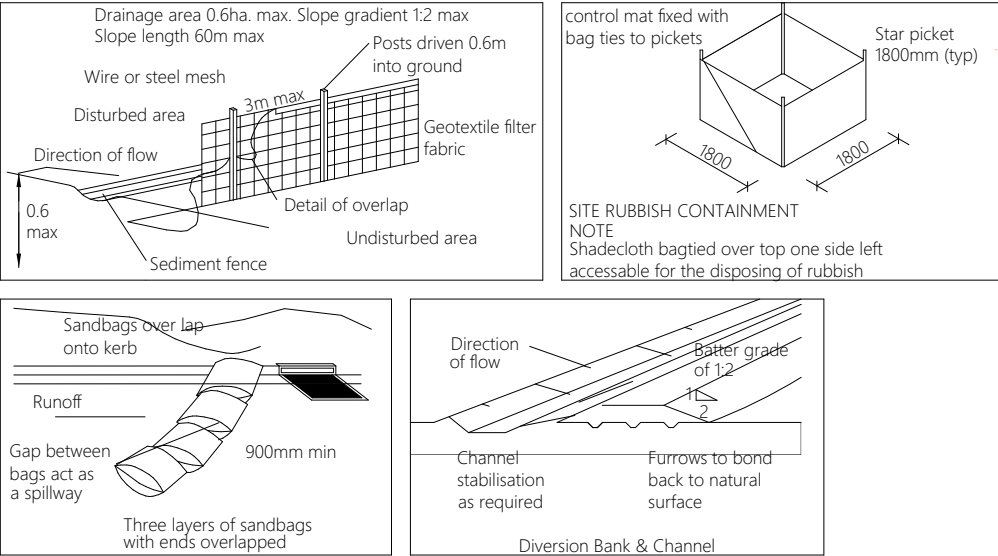

- NOTE
- 1 No vehicle crossing or stockpiling of material on vegetation buffer.
 - 2 All sedimentation control structures to be inspected & maintained by site manager daily.
 - 3 All sediment retaining structures to be cleaned on reaching 50% storage capacity.
 - 4 All existing vegetation will be retained outside the construction site.
 - 5 Clean sediments from footpaths, driveways & roads daily.
 - 6 Roof drainage via sealed pipeline to street gutter on roof completion.

NOTE:
THE LOCATION OF SERVICES ARE TO BE VERIFIED BY OBTAINING CURRENT INFORMATION FROM "DIAL BEFORE YOU DIG" (PHONE 1100) PRIOR TO DESIGN/CONSTRUCTION WORKS. ALTERNATIVELY, THE EXACT LOCATION OF SERVICES SHOULD BE DETERMINED BY FIELD SURVEY IN CONSULTATION WITH THE SERVICE AUTHORITIES WHERE DEEMED NECESSARY.

1	Cover Sheet	16	Builders Data
2	Site Analysis	17	Builders Data
3	Site Areas	18	3D Perspectives
4	Site Plan - Existing		
5	Site Plan - Proposed		
6	Ground Floor Plan - Existing		
7	First Floor Plan - Existing		
8	Ground Floor Plan - Proposed		
9	Elevations - Existing		
10	Elevations - Proposed		
11	Elevations - Proposed		
12	Section - Proposed		
13	Window Schedule		
14	Notification Plan		
15	Builders Data		



CONSTRUCTION PLANS

THESE PLANS HAVE BEEN ACCEPTED BY:

SIGNATURE:

DATE:

UPON ACCEPTANCE OF FINALISED CONSTRUCTION PLANS
NO FURTHER CHANGES ARE TO BE MADE TO ALLOW
APPLICATION SUBMISSION TO BE COMPLETED.

 DESIGN COLLECTIVE Phone: 0499 488 994 Email: matt@mtdesign.com.au ACN: 29 650 812 605	Rev. #	Drawn	Revision Details	Date	Client/s			Lot Number	Project Description		22137
	2	GK	CONCEPT PLANS	29.11.2022	Jaimie Moffitt			CP	Addition / Renovation		
	3	GK	CONCEPT AMENDMENT	07.12.2022				Drawing Name			
	4	GA	CONSTRUCTION PLANS	09.01.2022	Address 2/45 Curzon road New Lambton			DP	Cover Sheet		
	5	MD	DESIGN AMENDMENTS	08.03.2022				Drawing Status			
	6	MD	CONSTRUCTION PLANS	20.03.2023	Council Newcastle			State NSW	Postcode 2305	Submission Plans	1
	7	MD	CON. PLAN ADJ.	21.03.2023							
	8	MD	CERTIFIER RFI	30.03.2023							
	9	MD	CERTIFIER RFI	10.05.2023	THESE PLANS ARE DRAWN AND OWNED BY MT DESIGN COLLECTIVE AND ARE PROTECTED UNDER COPYRIGHT LAWS - PLANS ARE NOT TO BE COPIED OR RECREATED WITHOUT PRIOR WRITTEN CONSENT						

THESE PLANS ARE DRAWN AND OWNED BY MT DESIGN COLLECTIVE AND ARE PROTECTED UNDER COPYRIGHT LAWS - PLANS ARE NOT TO BE COPIED OR RECREATED WITHOUT PRIOR WRITTEN CONSENT


THE CITY OF NEWCASTLE

This plan/document is referred to in

Development Application No: DA2023/00424

The application has been consented to subject to compliance with conditions of consent.

Copyright: All documents have been reproduced by the City of Newcastle for the purposes of complying with its statutory obligations and may not be copied, used or otherwise reproduced in whole or in part without the authority of the copyright owner.

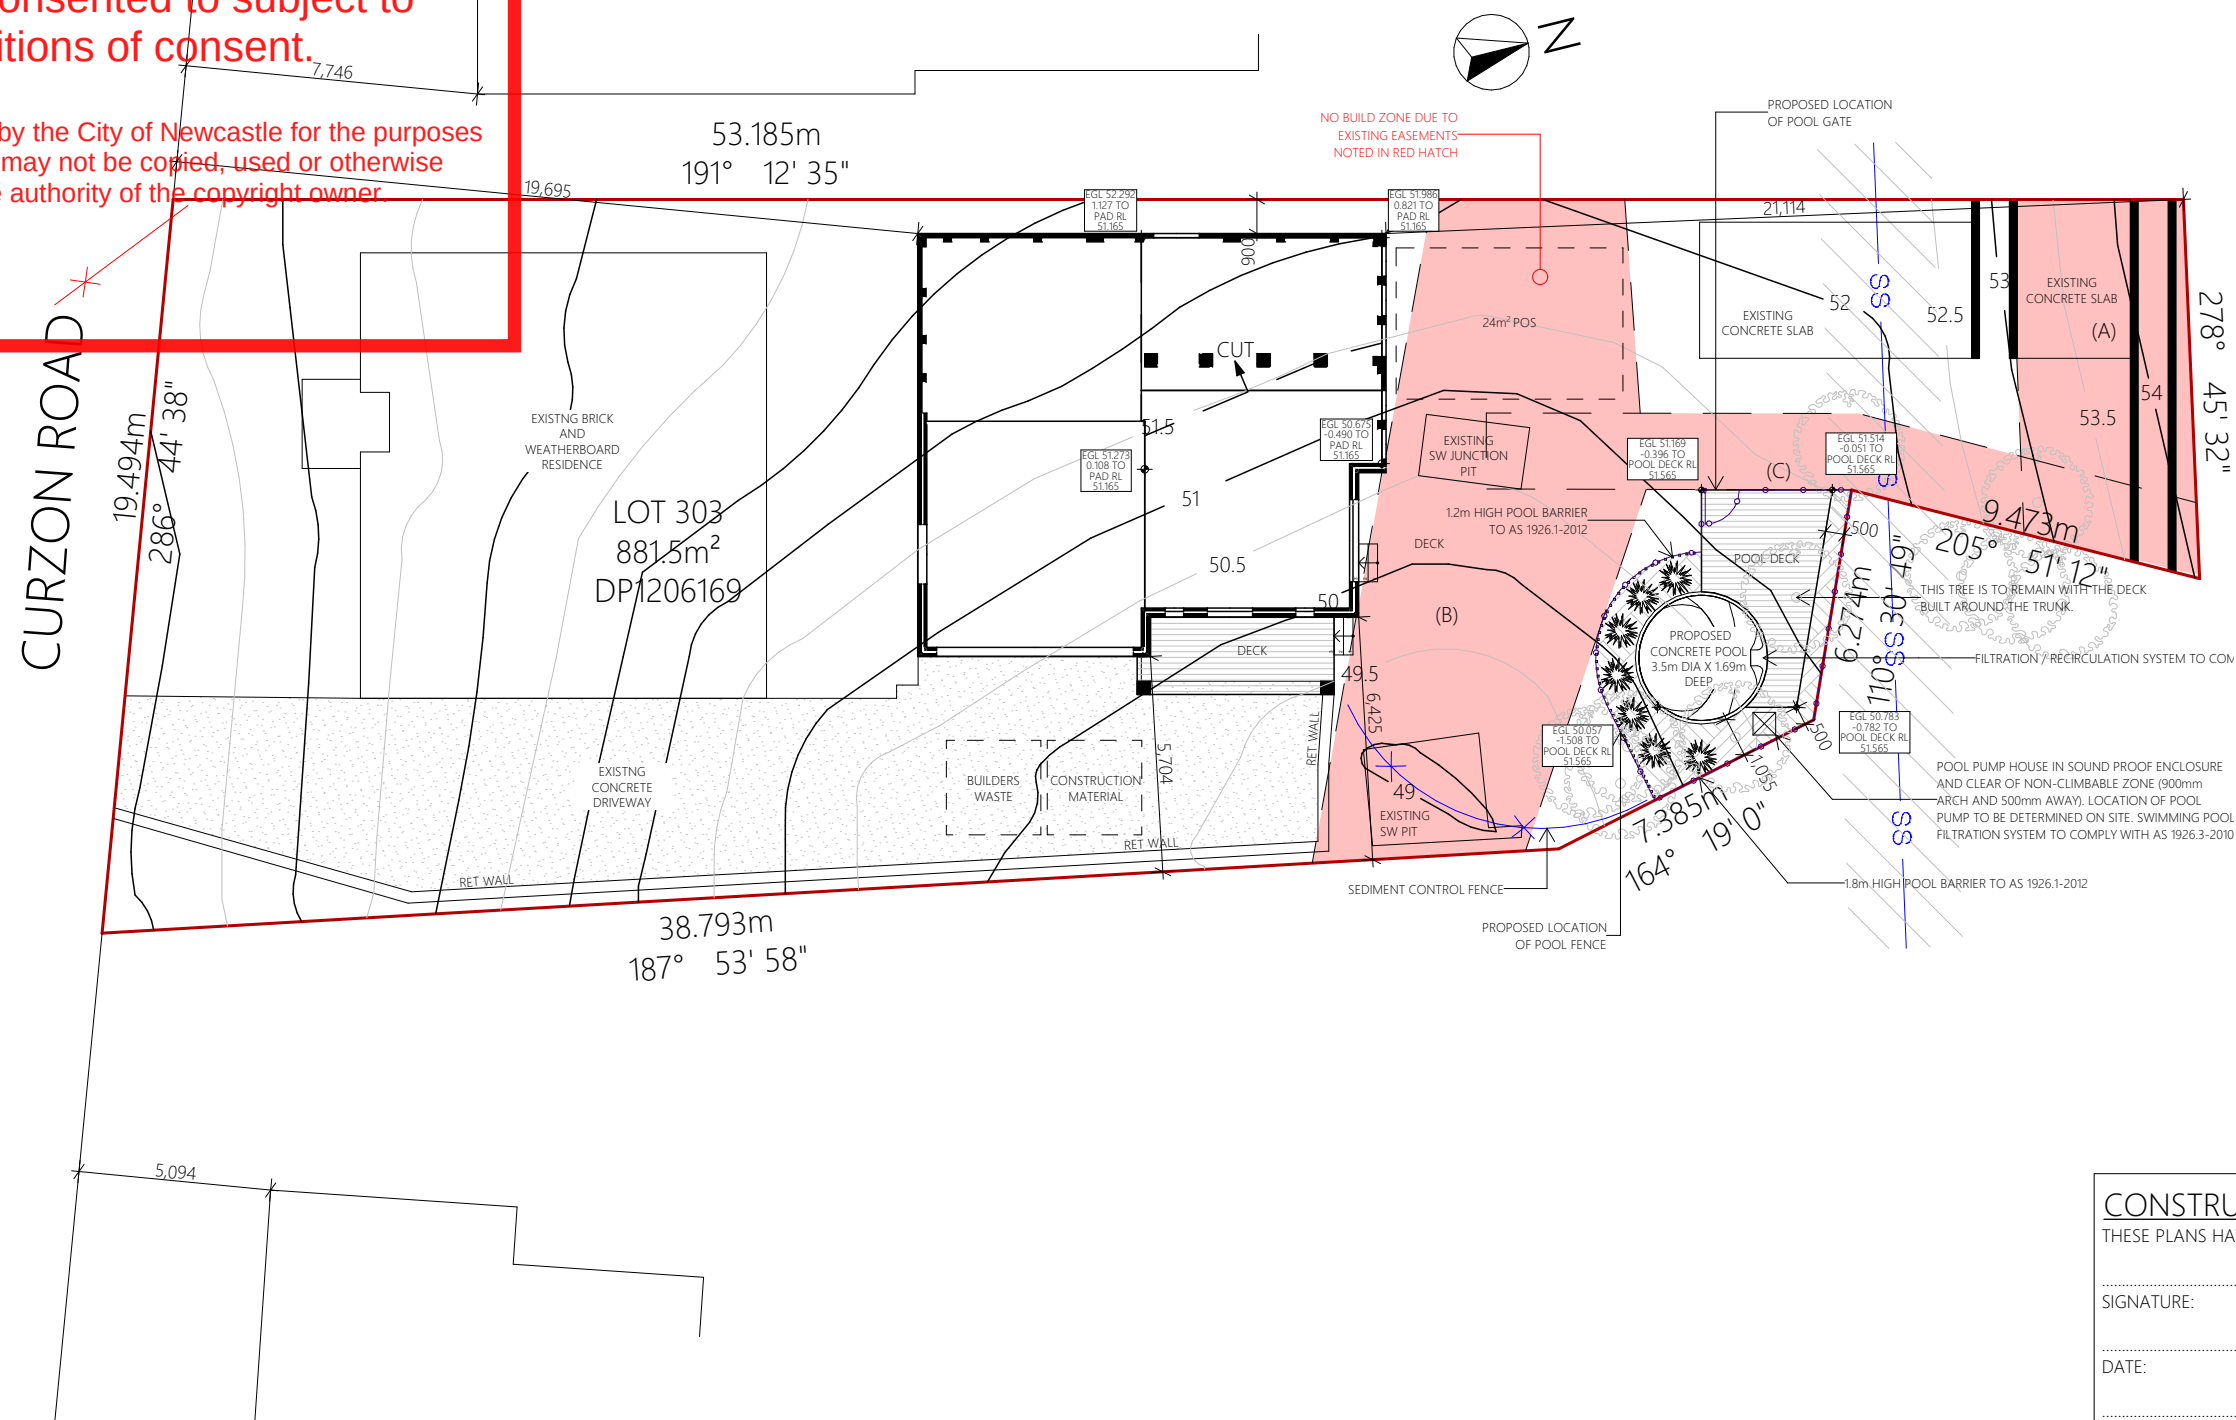

	PP	- POWER POLE
	PB	- POWER BOX
	SP	- SERVICE POLE
	LP	- LIGHT POLE
	HYD	- HYDRANT
	WM	- WATER METER
	SV	- STOP VALVE
	SMH	- SEWER MAINTENANCE HOLE
	SIO	- SEWER INSPECTION OPENING
	CPT	- TELECOMMUNICATIONS PIT
		- GAS METER
		- KERB INLET STORMWATER PIT
		- GRATED STORMWATER PIT
		- BENCHMARK
		- TREE

THESE PLANS HAVE BEEN ACCEPTED BY:

.....
SIGNATURE:

DATE: _____

UPON ACCEPTANCE OF FINALISED CONSTRUCTION PLANS
NO FURTHER CHANGES ARE TO BE MADE TO ALLOW
APPLICATION SUBMISSION TO BE COMPLETED.



Rev. #	Drawn	Revision Details	Date	Client/s			Lot Number	Project Description		22137
2	GK	CONCEPT PLANS	29.11.2022	Jaimie Moffitt			CP	Addition / Renovation		
3	GK	CONCEPT AMENDMENT	07.12.2022							
4	GA	CONSTRUCTION PLANS	09.01.2022	Address 2/45 Curzon road New Lambton			DP SP99543	Drawing Name Site Plan - Proposed		
5	MD	DESIGN AMENDMENTS	08.03.2022							
6	MD	CONSTRUCTION PLANS	20.03.2023							
7	MD	CON. PLAN ADJ.	21.03.2023	Council Newcastle	State NSW	Postcode 2305	Drawing Scale 1:200	Drawing Status Submission Plans		5
8	MD	CERTIFIER RFI	30.03.2023							
9	MD	CERTIFIER RFI	10.05.2023							

THESE PLANS ARE DRAWN AND OWNED BY MT DESIGN COLLECTIVE AND ARE PROTECTED UNDER COPYRIGHT LAWS - PLANS ARE NOT TO BE COPIED OR RECREATED WITHOUT PRIOR WRITTEN CONSENT

THESE PLANS ARE DRAWN AND OWNED BY MT DESIGN COLLECTIVE AND ARE PROTECTED UNDER COPYRIGHT LAWS - PLANS ARE NOT TO BE COPIED OR RECREATED WITHOUT PRIOR WRITTEN CONSENT


THE CITY OF NEWCASTLE

This plan/document is referred to in


Development Application No: DA2023/00424

The application has been consented to subject to compliance with conditions of consent.


Copyright: All documents have been reproduced by the City of Newcastle for the purposes of complying with its statutory obligations and may not be copied, used or otherwise reproduced in whole or in part without the authority of the copyright owner.

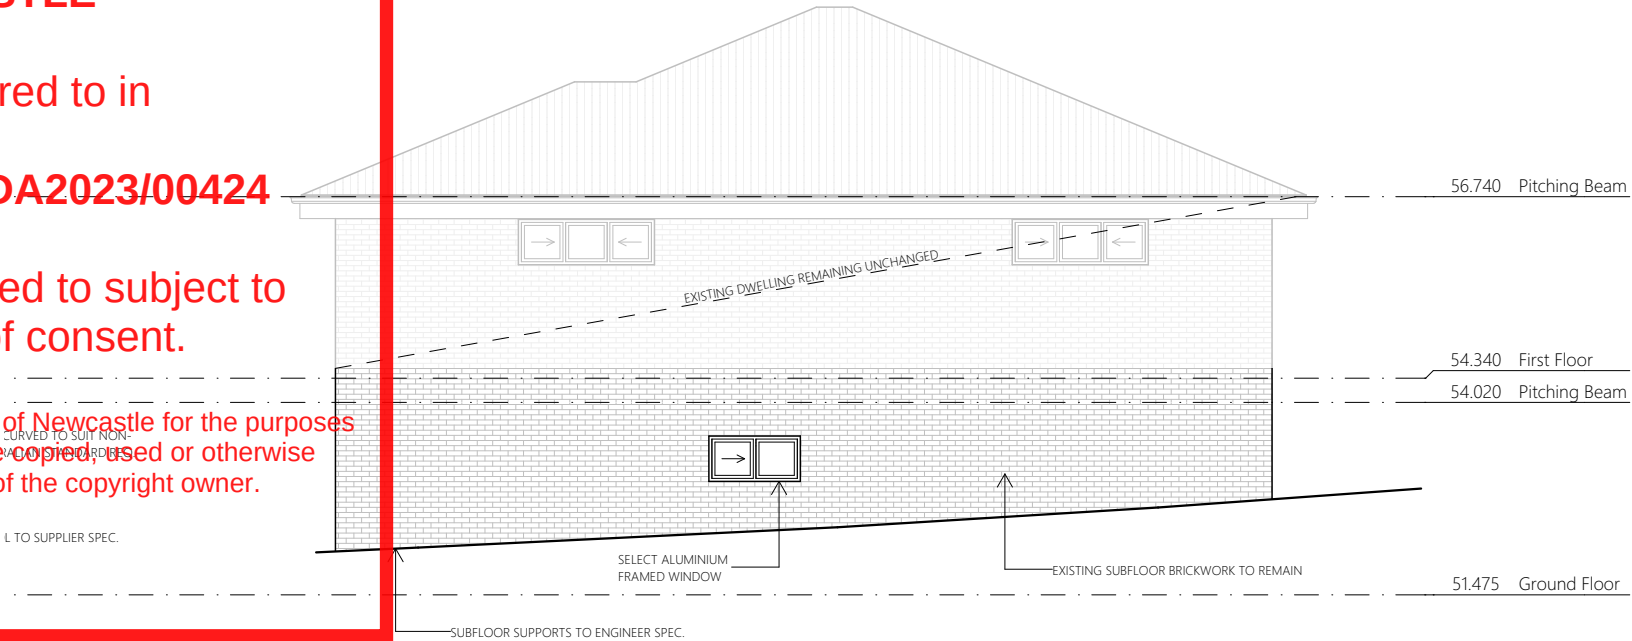

E01 Elevation 1:100

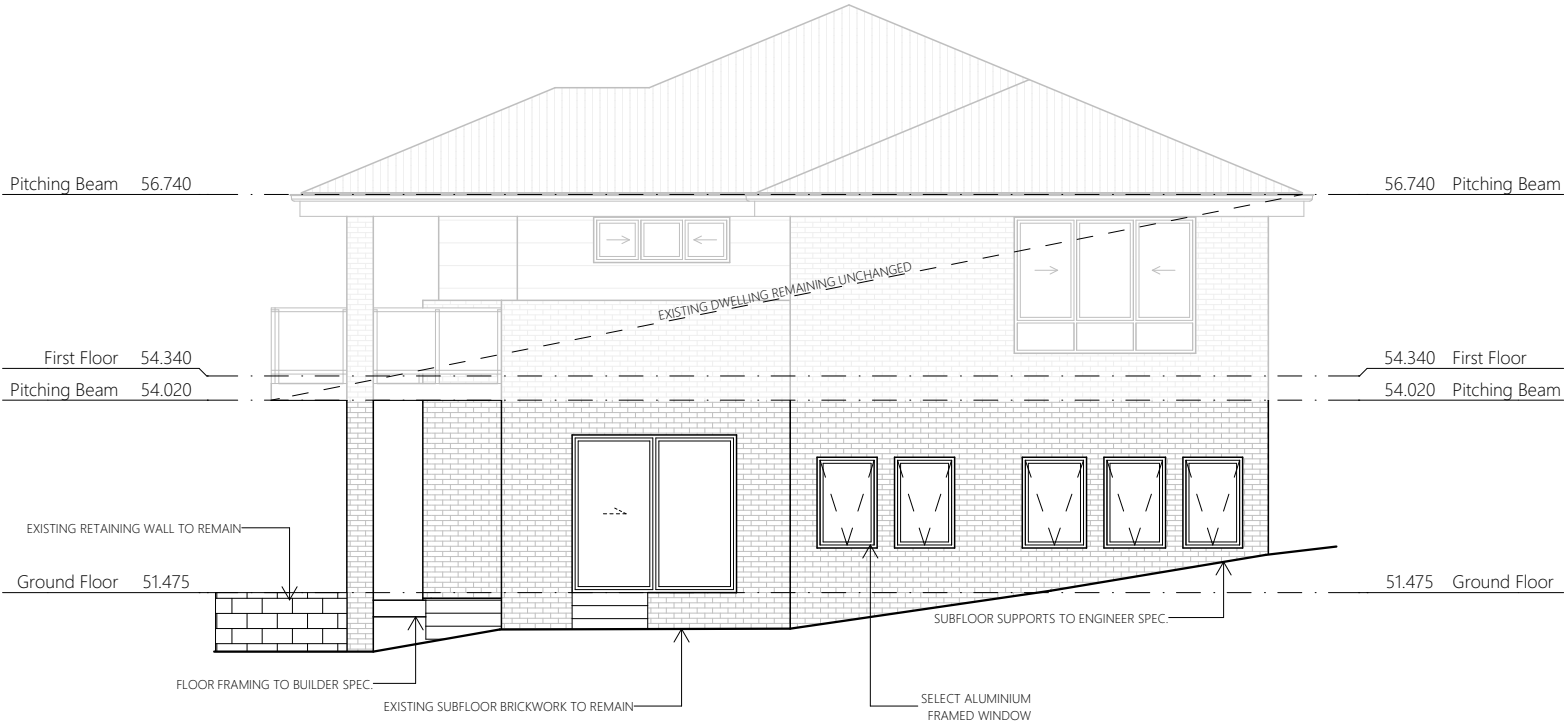

E02 Elevation 1:100

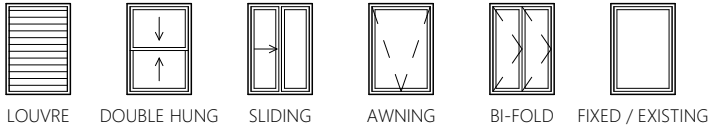

CONSTRUCTION PLANS

THESE PLANS HAVE BEEN ACCEPTED BY:

SIGNATURE:

DATE:

UPON ACCEPTANCE OF FINALISED CONSTRUCTION PLANS NO FURTHER CHANGES ARE TO BE MADE TO ALLOW APPLICATION SUBMISSION TO BE COMPLETED.



Rev. #	Drawn	Revision Details	Date	Client/s			Lot Number	Project Description	22137
2	GK	CONCEPT PLANS	29.11.2022	Jaimie Moffitt			CP	Addition / Renovation	
3	GK	CONCEPT AMENDMENT	07.12.2022						
4	GA	CONSTRUCTION PLANS	09.01.2022						
5	MD	DESIGN AMENDMENTS	08.03.2022	Address 2/45 Curzon road New Lambton			DP SP99543	Drawing Name Elevations - Proposed	
6	MD	CONSTRUCTION PLANS	20.03.2023						
7	MD	CON. PLAN ADJ.	21.03.2023	Council Newcastle	State NSW	Postcode 2305	Drawing Scale 1:100	Drawing Status Submission Plans	10
8	MD	CERTIFIER RFI	30.03.2023						
9	MD	CERTIFIER RFI	10.05.2023						

THESE PLANS ARE DRAWN AND OWNED BY MT DESIGN COLLECTIVE AND ARE PROTECTED UNDER COPYRIGHT LAWS - PLANS ARE NOT TO BE COPIED OR RECREATED WITHOUT PRIOR WRITTEN CONSENT

THE CITY OF NEWCASTLE

This plan/document is referred to in

Development Application No: DA2023/00424

The application has been consented to subject to
compliance with conditions of consent.

Copyright: All documents have been reproduced by the City of Newcastle for the purposes
of complying with its statutory obligations and may not be copied, used or otherwise
reproduced in whole or in part without the authority of the copyright owner.

An architectural drawing of a building facade with a pitched roof. The drawing shows a section of the building with several windows. Some windows have arrows indicating they are open or closed. The drawing is partially obscured by text overlays.

Development Application No: DA2023/00424

Pitching Beam 56.740

with conditions

Pitching Beam	54.020
---------------	--------

Ground Floor 51.475

FLOOR FRAMING TO BUILDER SPEC _____

EXISTING RETAINING WALL TO REMAIN

—TIMBER STAIRS TO BUILDER SPEC


1.2m HIGH POOL FENCING CURVED TO SUIT NON-CLIMABLE ZONE PER AUSTRALIAN STANDARD REQ.

—1.2m HIGH POOL FENCING

FLOOR FRAMING

—EXPOSED EDGE OF CONCRETE POOL

1:100

 

ED / EXISTING

UPON ACCEPTANCE OF FINALISED CONSTRUCTION PLANS
NO FURTHER CHANGES ARE TO BE MADE TO ALLOW
APPLICATION SUBMISSION TO BE COMPLETED.



Rev. #	Drawn	Revision Details	Date	Client/s			Lot Number	Project Description	22137
2	GK	CONCEPT PLANS	29.11.2022	Jaimie Moffitt			CP	Addition / Renovation	
3	GK	CONCEPT AMENDMENT	07.12.2022						
4	GA	CONSTRUCTION PLANS	09.01.2022	Address 2/45 Curzon road New Lambton			DP SP99543	Drawing Name Elevations - Proposed	
5	MD	DESIGN AMENDMENTS	08.03.2022						
6	MD	CONSTRUCTION PLANS	20.03.2023	Council Newcastle			Drawing Scale 1:100	Drawing Status Submission Plans	11
7	MD	CON. PLAN ADJ.	21.03.2023						
8	MD	CERTIFIER RFI	30.03.2023						
9	MD	CERTIFIER RFI	10.05.2023	State NSW			Postcode 2305		

THESE PLANS ARE DRAWN AND OWNED BY MT DESIGN COLLECTIVE AND ARE PROTECTED UNDER COPYRIGHT LAWS - PLANS ARE NOT TO BE COPIED OR RECREATED WITHOUT PRIOR WRITTEN CONSENT



THE CITY OF NEWCASTLE

This plan/document is referred to in

Development Application No: DA2023/00424

The application has been consented to subject to compliance with conditions of consent.

Copyright: All documents have been reproduced by the City of Newcastle for the purposes of complying with its statutory obligations and may not be copied, used or otherwise reproduced in whole or in part without the authority of the copyright owner.

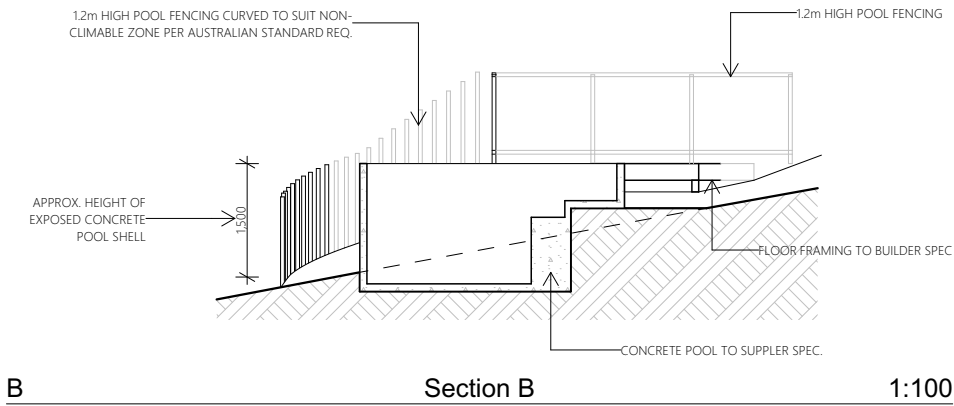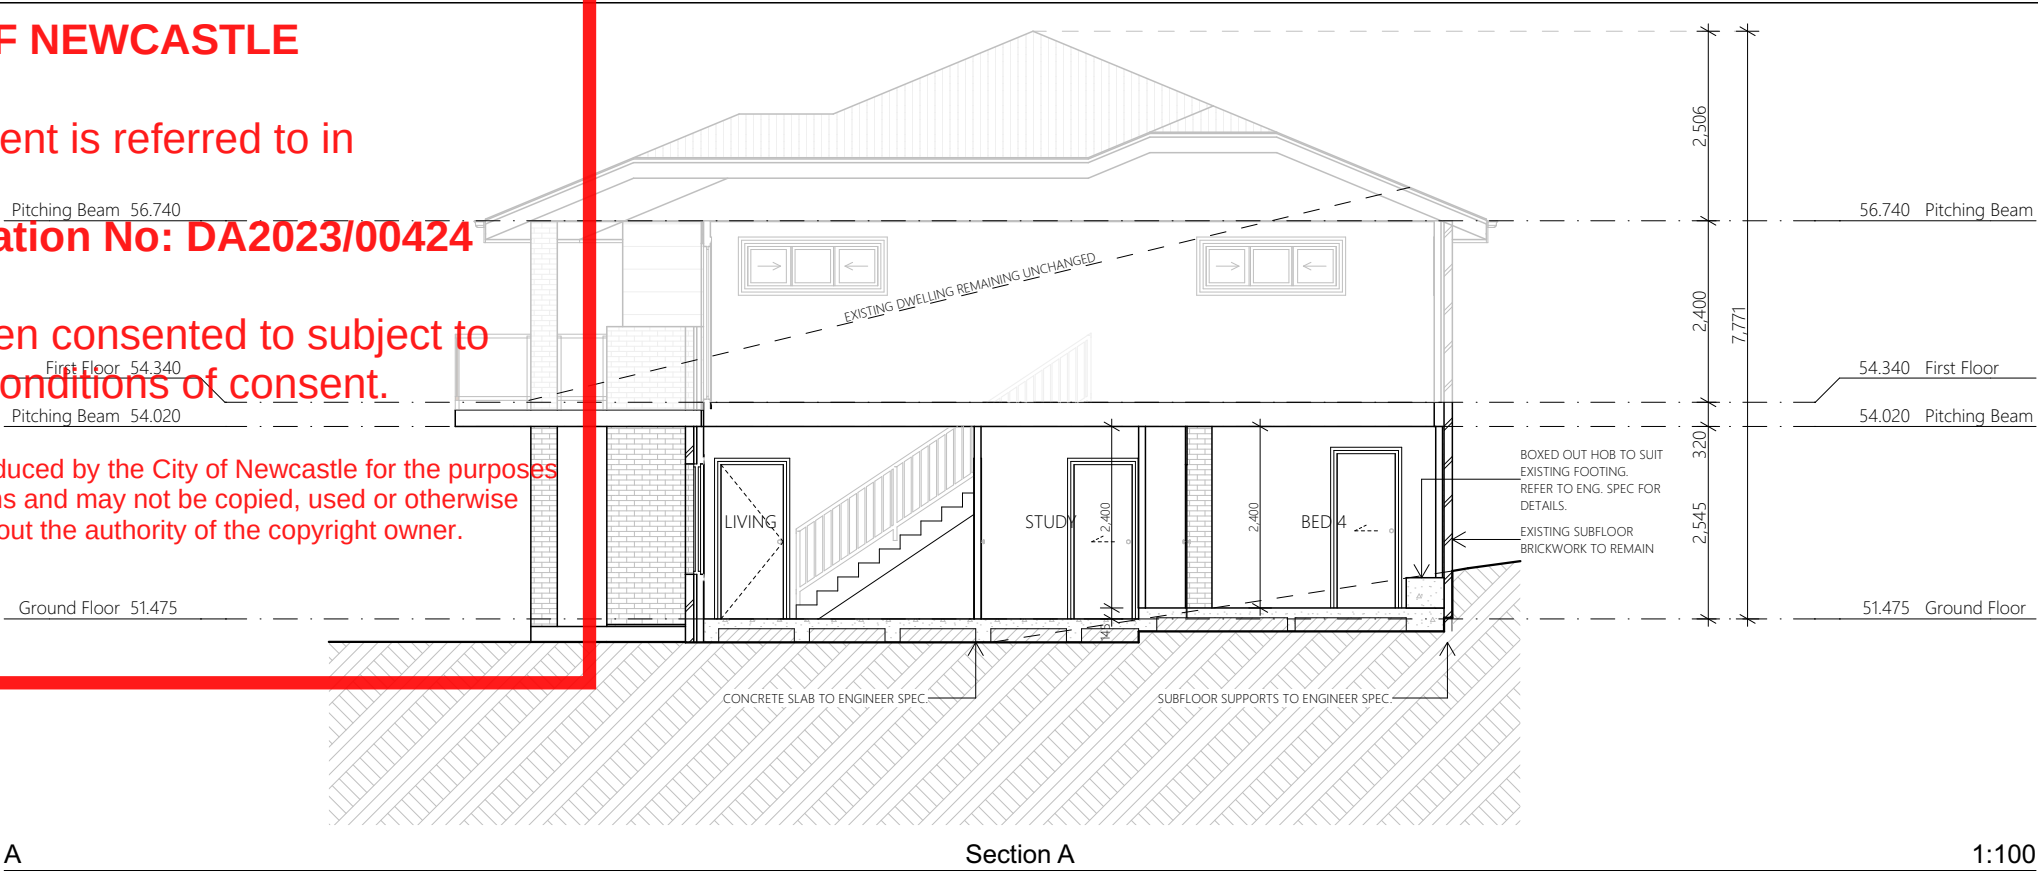

CONSTRUCTION PLANS
THESE PLANS HAVE BEEN ACCEPTED BY:

SIGNATURE: _____

DATE: _____

UPON ACCEPTANCE OF FINALISED CONSTRUCTION PLANS
NO FURTHER CHANGES ARE TO BE MADE TO ALLOW
APPLICATION SUBMISSION TO BE COMPLETED.

 DESIGN COLLECTIVE Phone: 0499 488 994 Email: matt@mtdesign.com.au ACN: 29 650 812 605	Rev. #	Drawn	Revision Details	Date	Client/s			Lot Number	Project Description		22137	
	2	GK	CONCEPT PLANS	29.11.2022	Jaimie Moffitt			CP	Addition / Renovation			
	3	GK	CONCEPT AMENDMENT	07.12.2022	Address 2/45 Curzon road New Lambton			DP SP99543	Drawing Name	Section - Proposed		
	4	GA	CONSTRUCTION PLANS	09.01.2022								
	5	MD	DESIGN AMENDMENTS	08.03.2022				Drawing Scale 1:100	Drawing Status	Submission Plans		
	6	MD	CONSTRUCTION PLANS	20.03.2023	Council Newcastle	State NSW	Postcode 2305					
	7	MD	CON. PLAN ADJ.	21.03.2023								
	8	MD	CERTIFIER RFI	30.03.2023								
	9	MD	CERTIFIER RFI	10.05.2023								

THESE PLANS ARE DRAWN AND OWNED BY MT DESIGN COLLECTIVE AND ARE PROTECTED UNDER COPYRIGHT LAWS - PLANS ARE NOT TO BE COPIED OR RECREATED WITHOUT PRIOR WRITTEN CONSENT