


Proposed Roof & Stormwater Plan - Alts and Additions

Scale 1:200

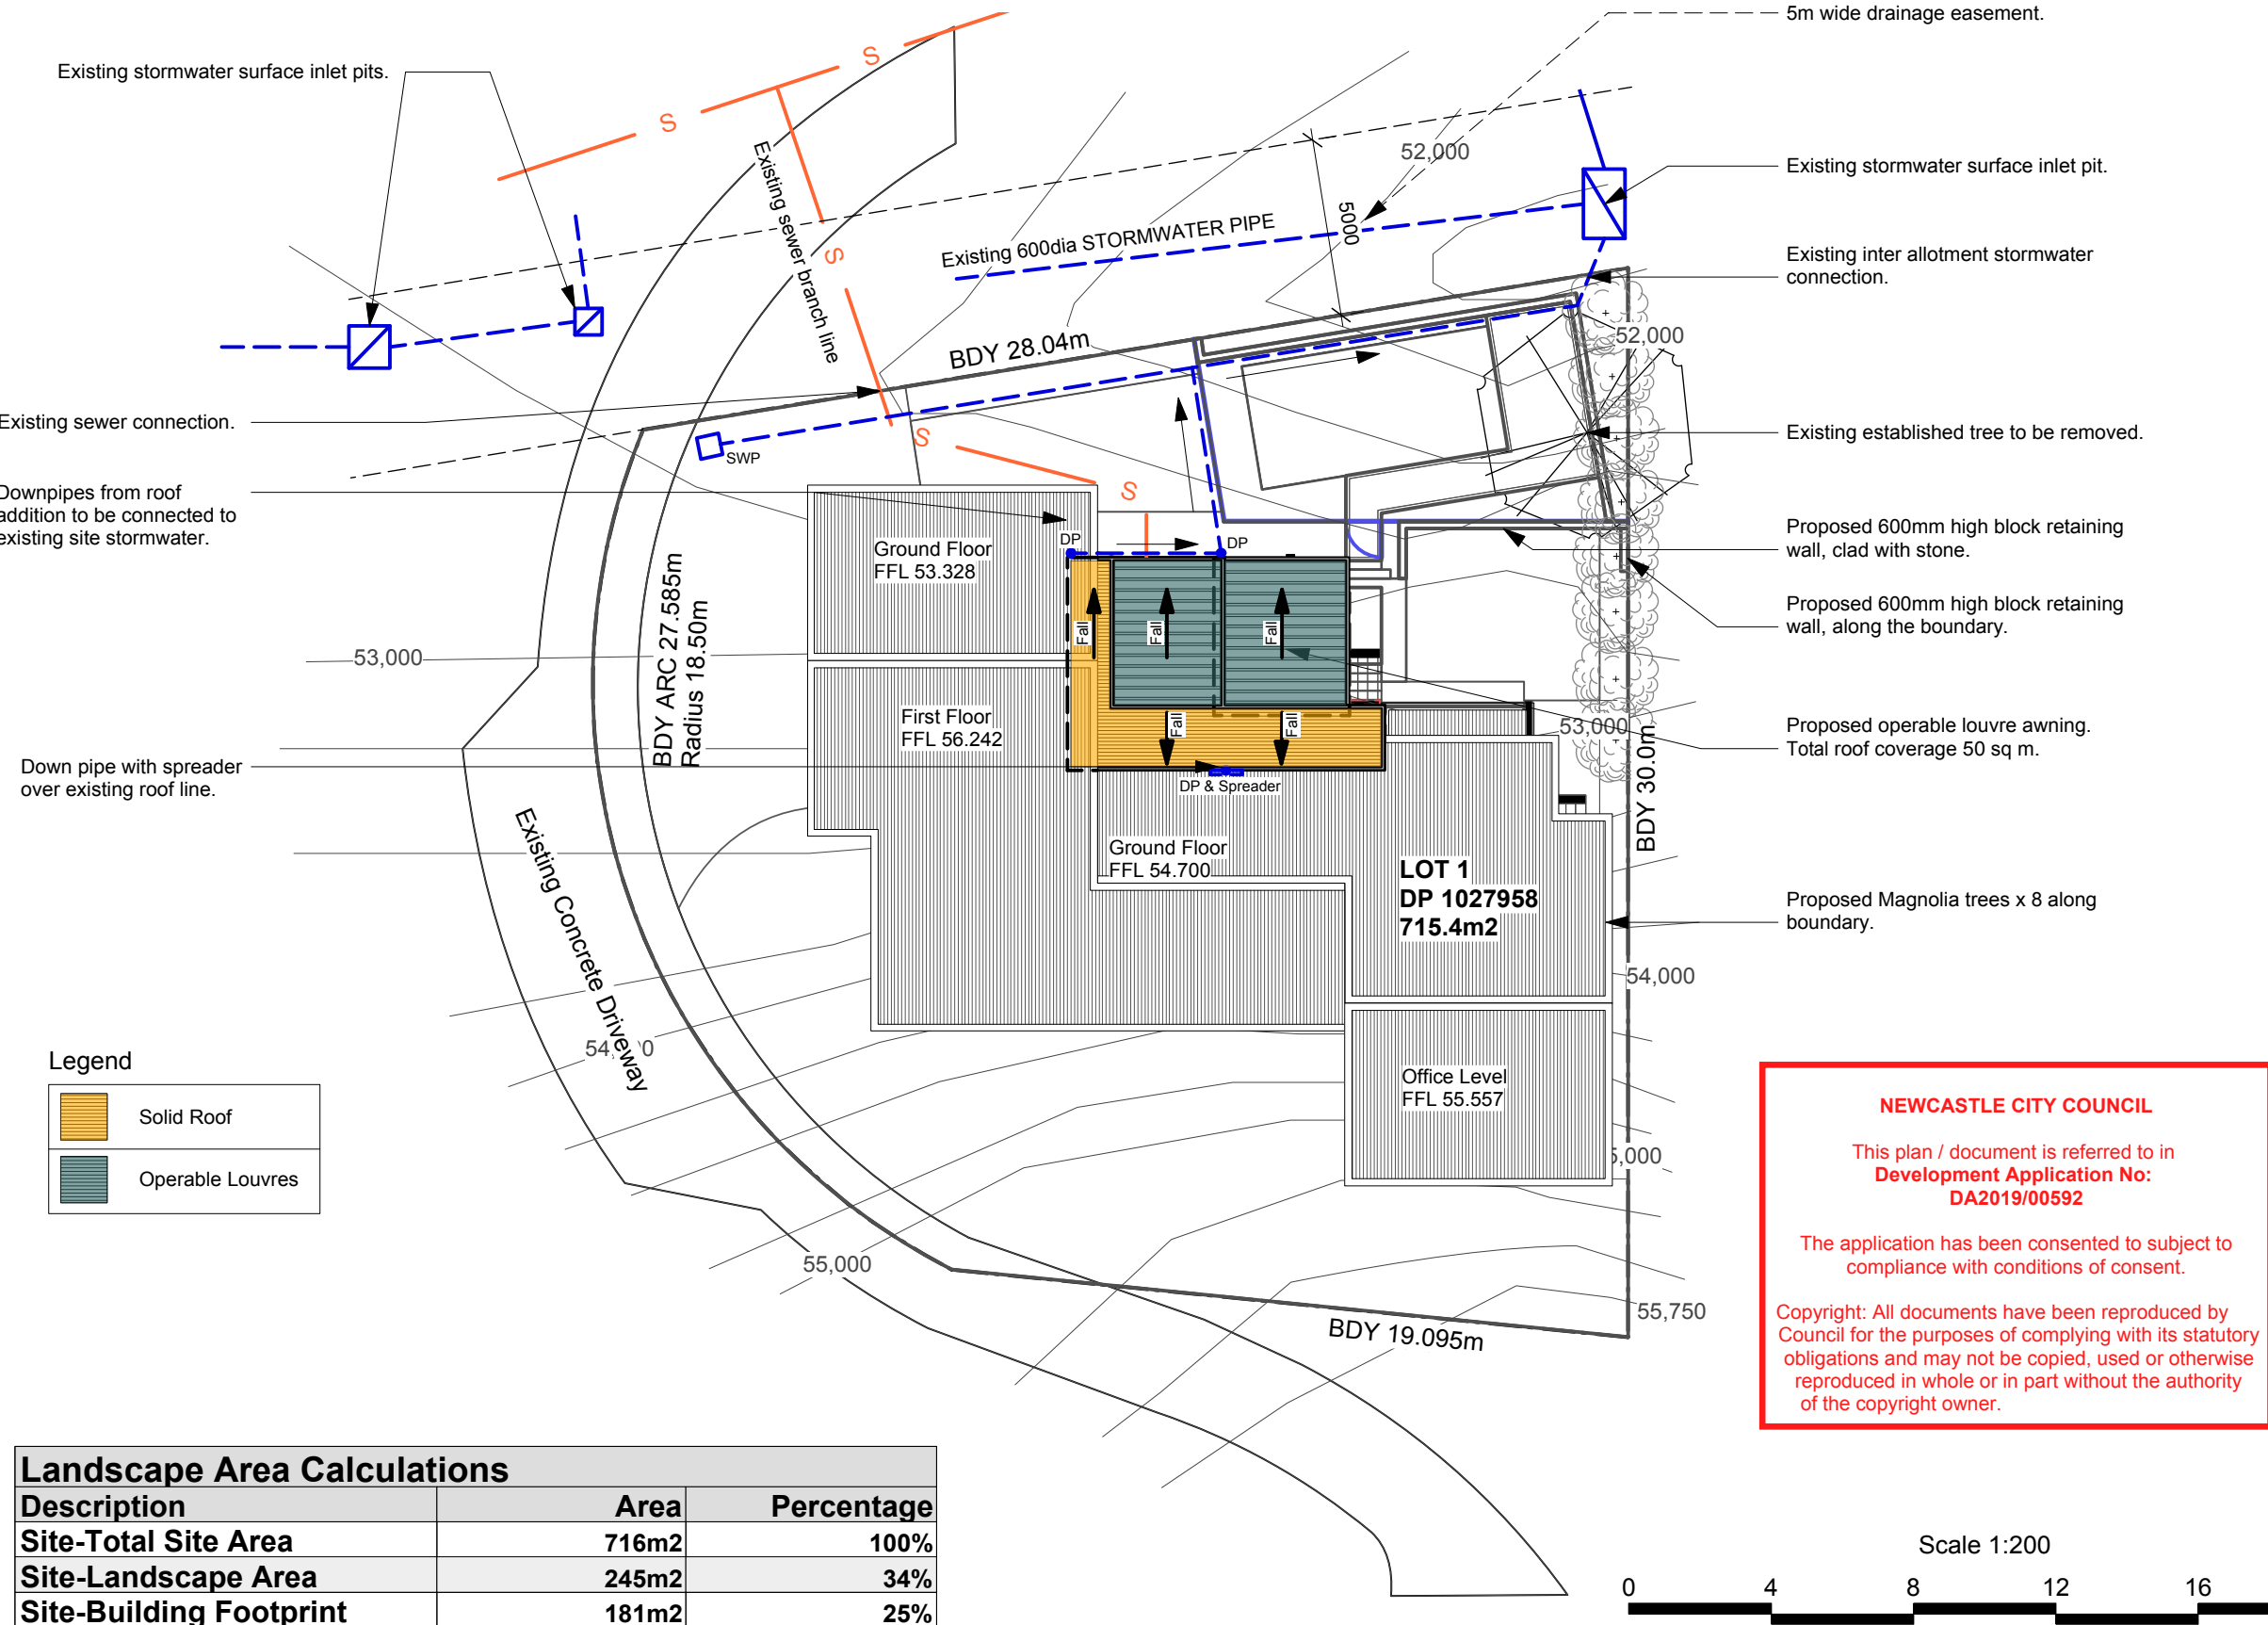


Existing Site Photos

Landscape Area Calculations		
Description	Area	Percentage
Site-Total Site Area	716m2	100%
Site-Landscape Area	245m2	34%
Site-Building Footprint	181m2	25%
Site-Proposed Roof Awning	46m2	6%


Landscape DA Documentation


Demolition Plan - Proposed Alts & Adds

Scale 1:100

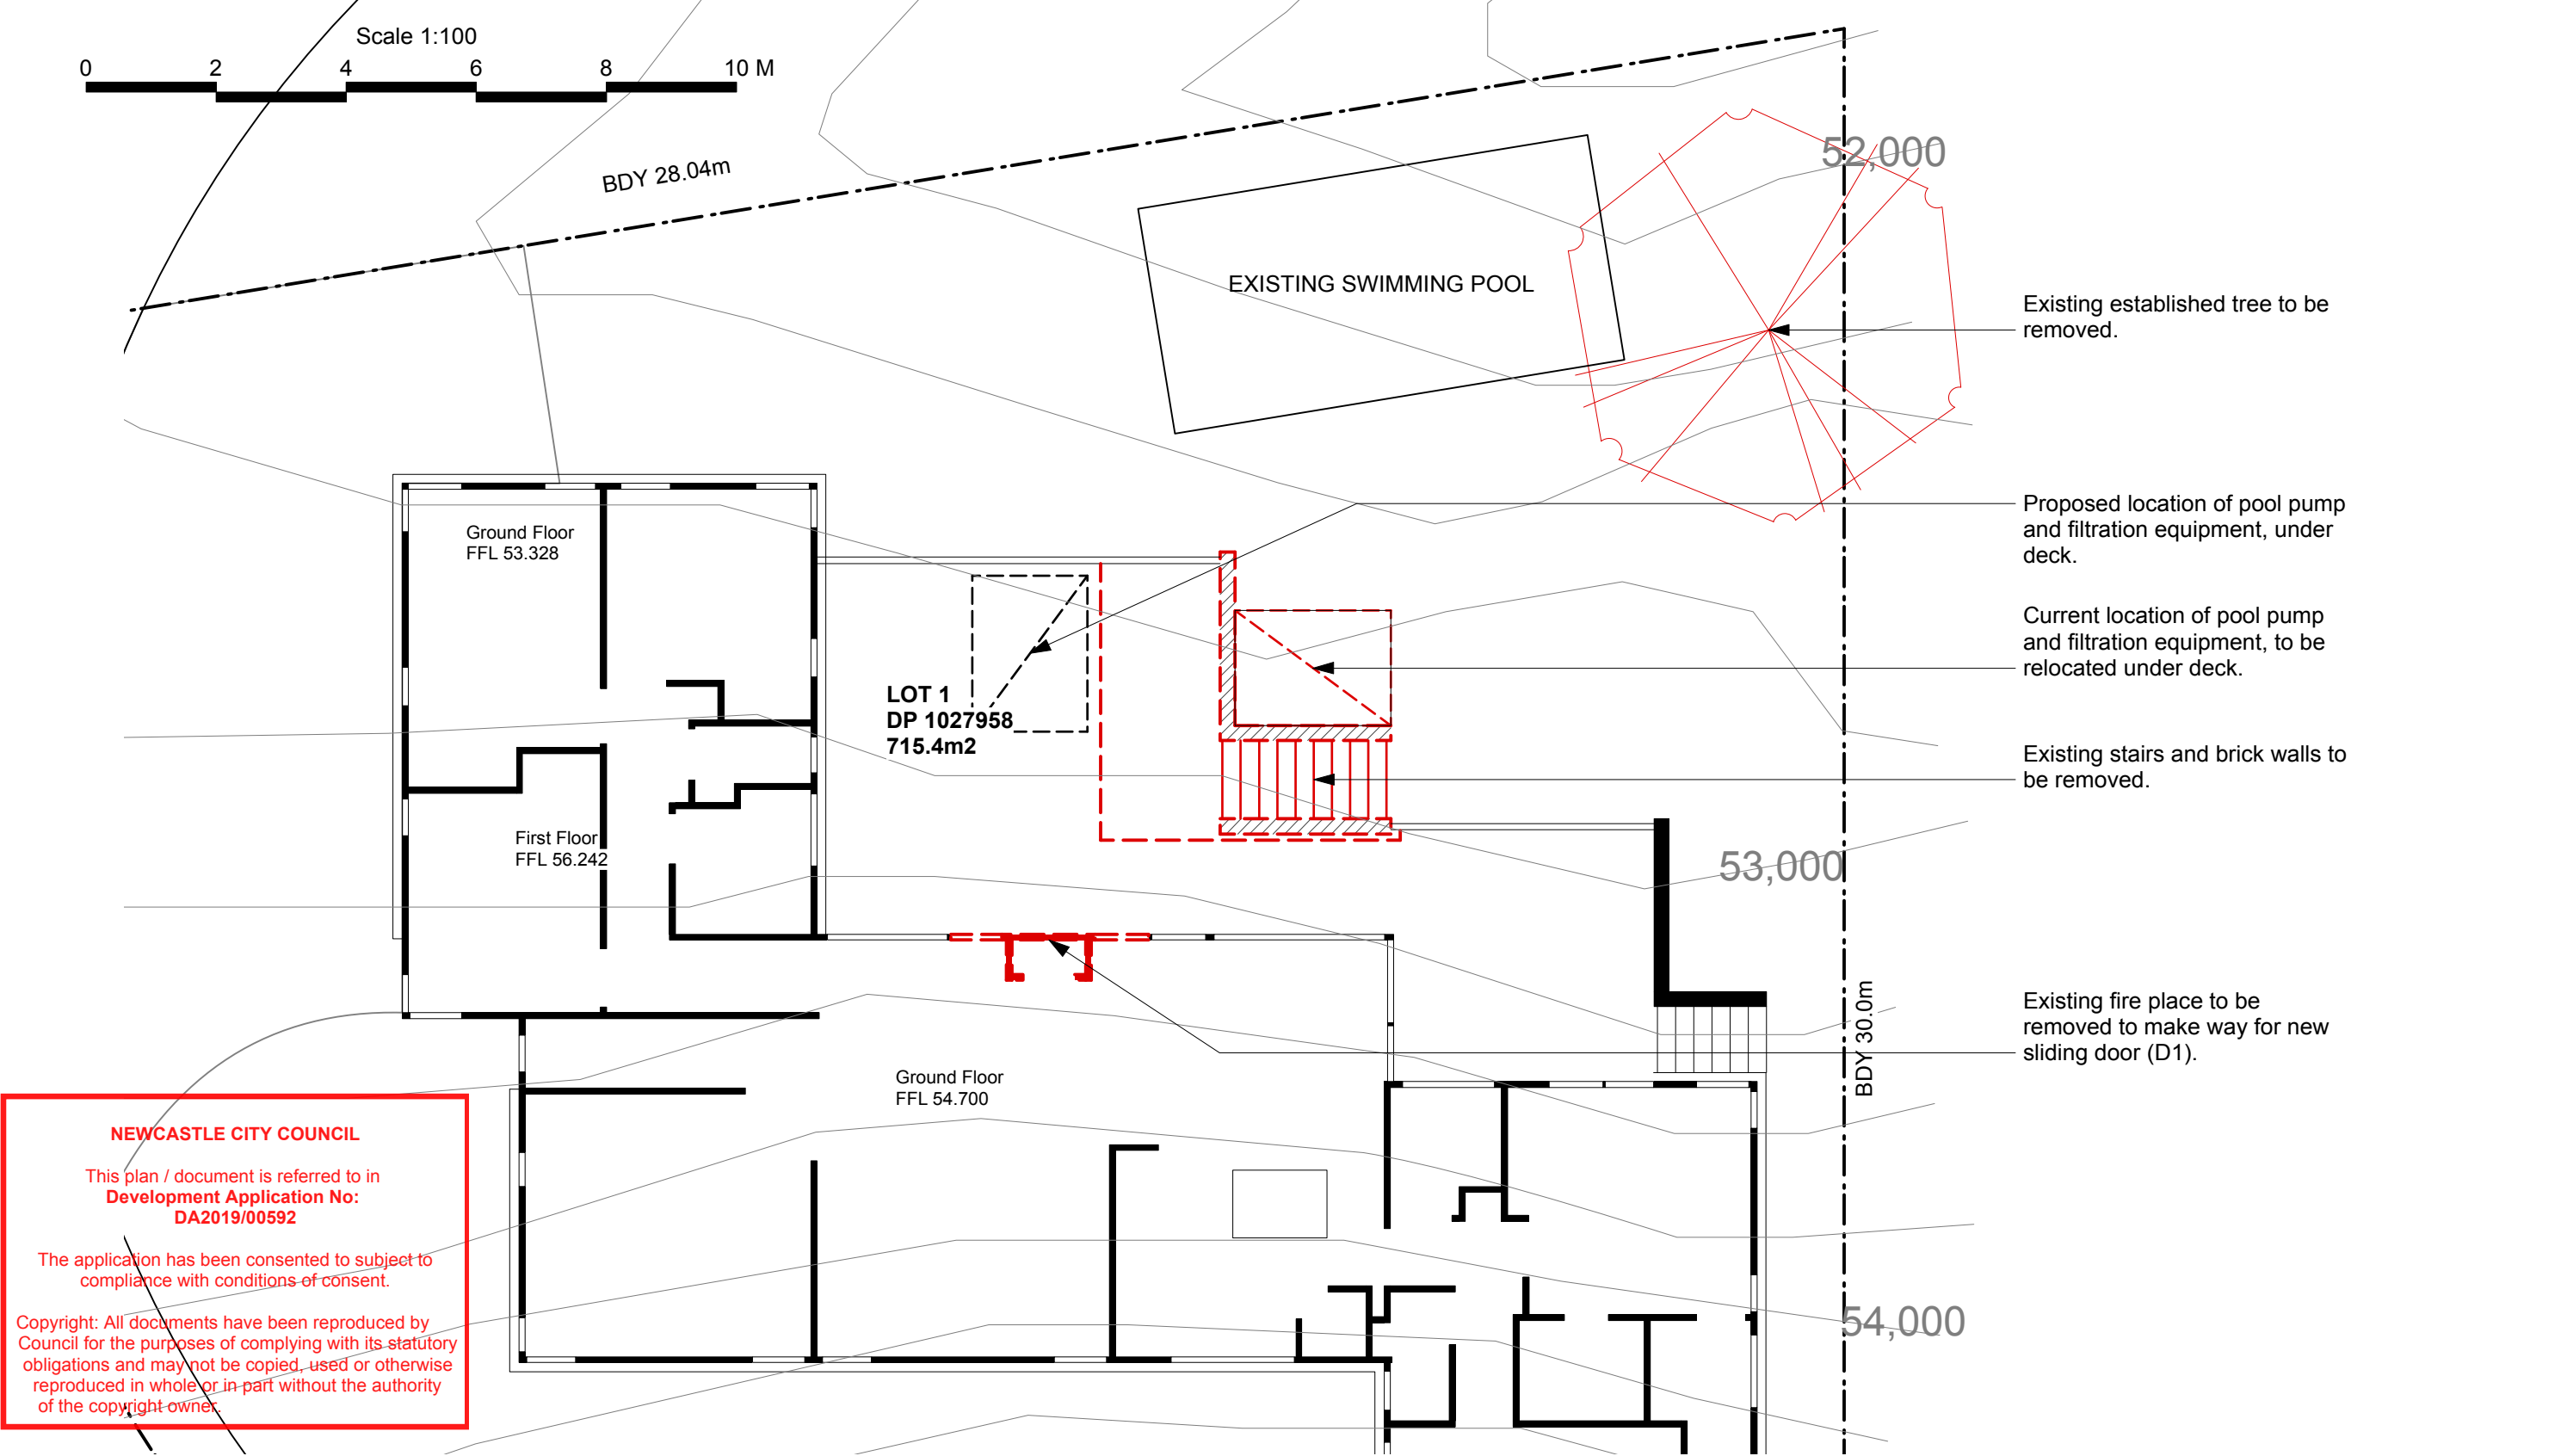


Landscape DA Documentation

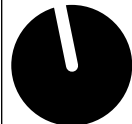	DESIGN STUDIO MUD LANDSCAPE DESIGN The Roost, Level 1 152 - 158 Hunter Street, Newcastle, NSW, 2300 Phone 0415 883 167 Email hello@mud.design	 AILDM Australian Institute of Landscape Designers and Managers Member No: 1355	A	15/11/18	1.0 Preliminary Landscape Concept Design	All	MT	Project Manager Mark Tisdell	PROJECT ID: 0419WitherdinCurzon	SITE: 47a Curzon Road New Lambton, NSW, 2305	WORK TO FIGURED DIMENSIONS IN PREFERENCE TO SCALE. CHECK DIMENSIONS AND LEVELS ON SITE BEFORE ORDERING MATERIALS OR THE COMPLETION OF WORKSHOP DRAWINGS		Drawing: Demolition Plan
			B	11/12/18	2.0 Landscape Concept Design	All	MT	Drawn By Mark Tisdell					
			C	11/06/19	DA Documentation - Revision 1	All	MT	Reviewed By Julia Jerome					
						Date 11/06/19							
						CAD File Name 1.0 4418WWitherdinCurzon.vwx							
									CLIENT: Amber & David Witherdin	ISSUE: Landscape DA Documentation			
									Print date: 11/06/19		Scale @ A3: 1:100	Page no. 2.03	

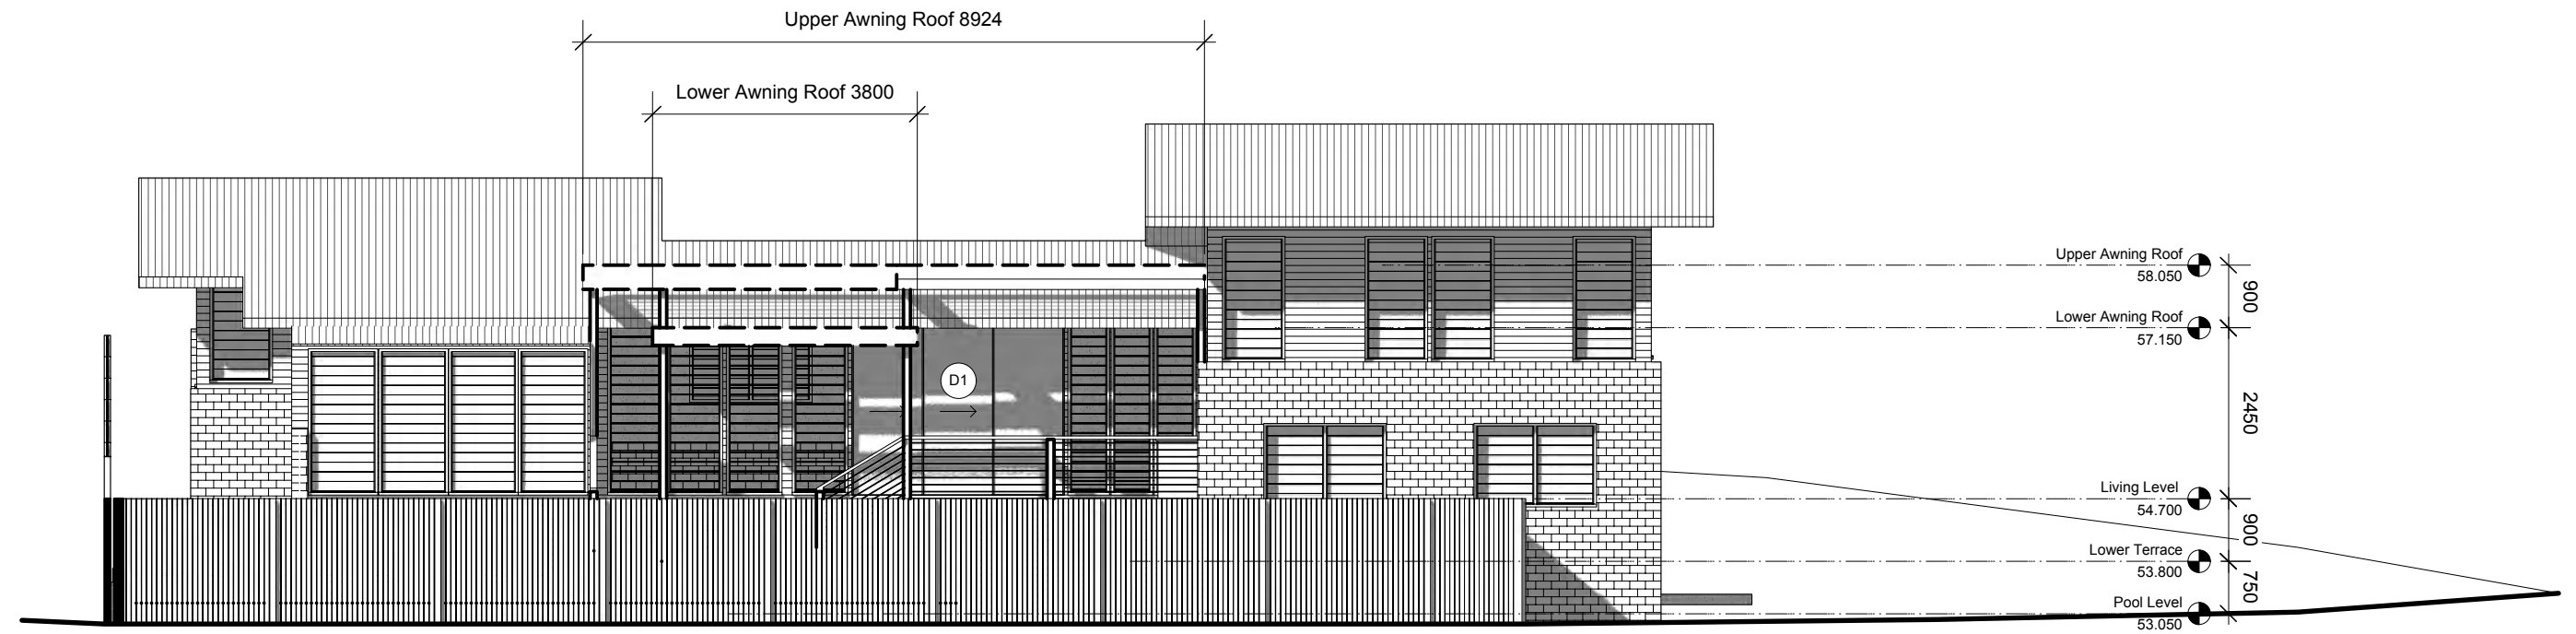

North Elevation - Proposed Pergola Structure

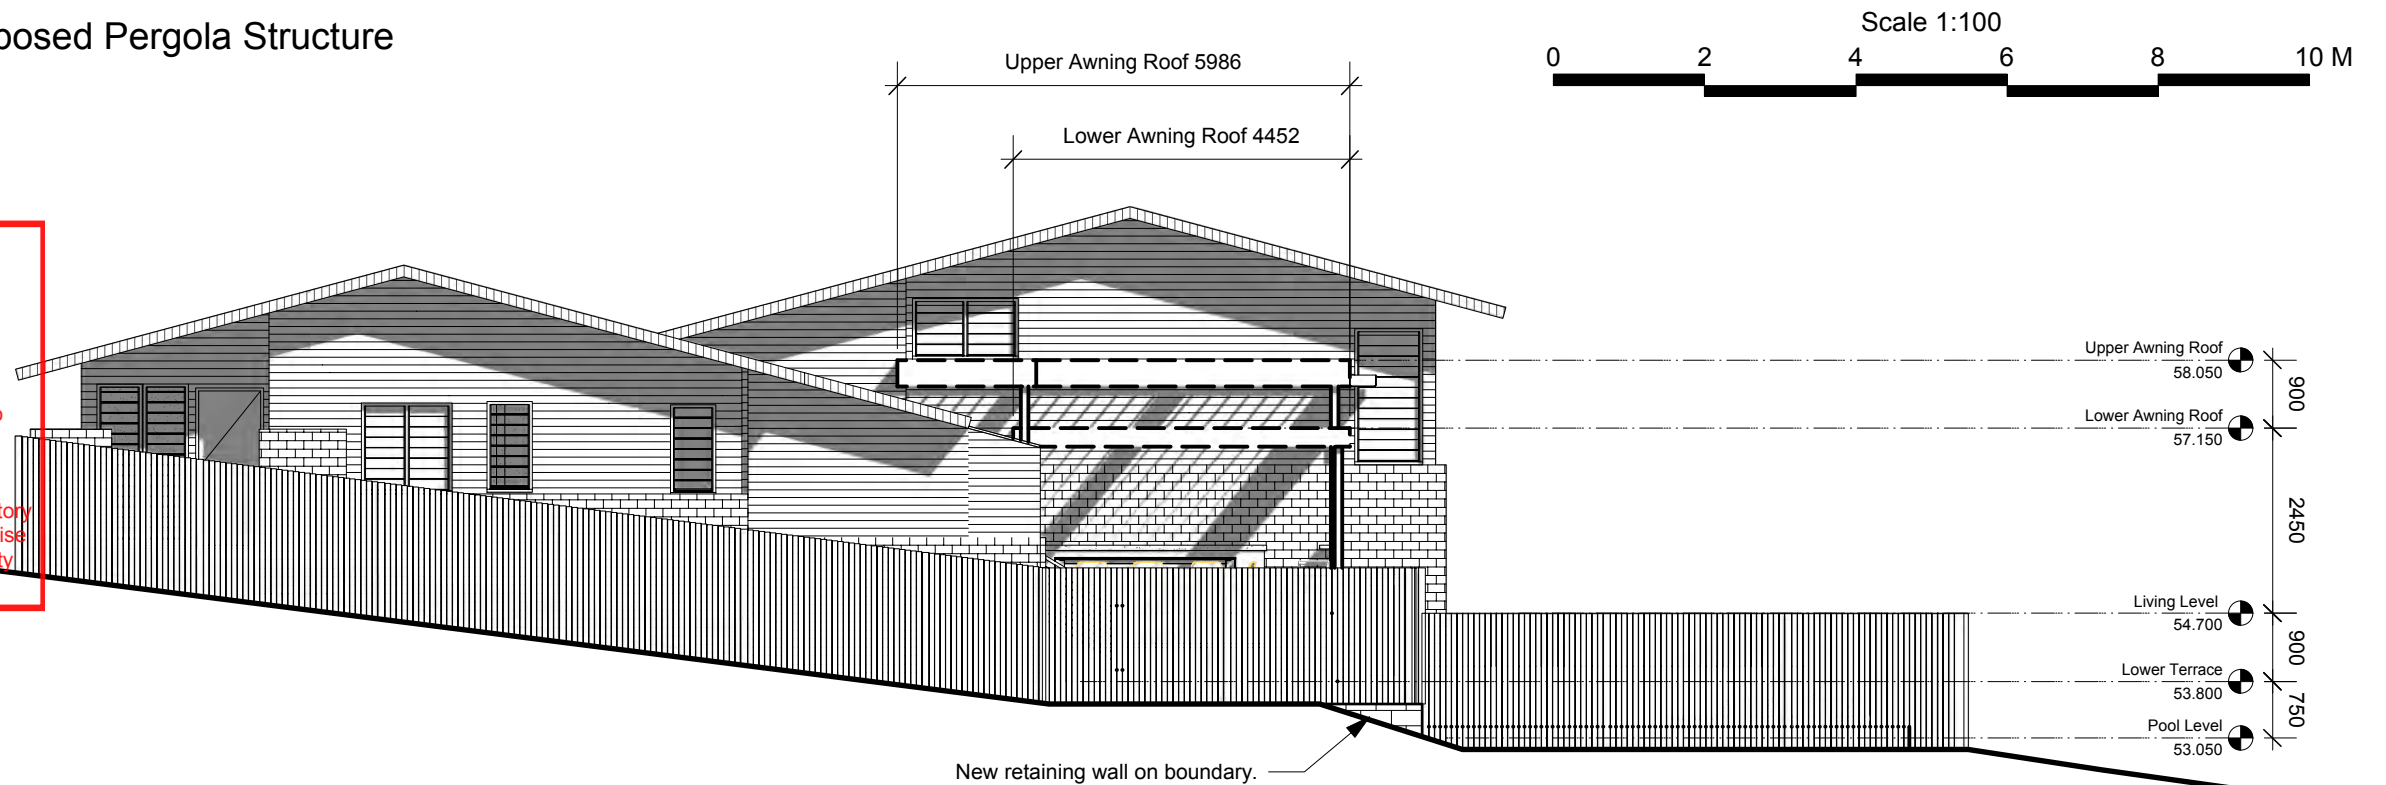

East Elevation - Proposed Pergola Structure


Scale 1:100

NEWCASTLE CITY COUNCIL

This plan / document is referred to in
Development Application No:
DA2019/00592

The application has been consented to subject to compliance with conditions of consent.

Copyright: All documents have been reproduced by Council for the purposes of complying with its statutory obligations and may not be copied, used or otherwise reproduced in whole or in part without the authority of the copyright owner.

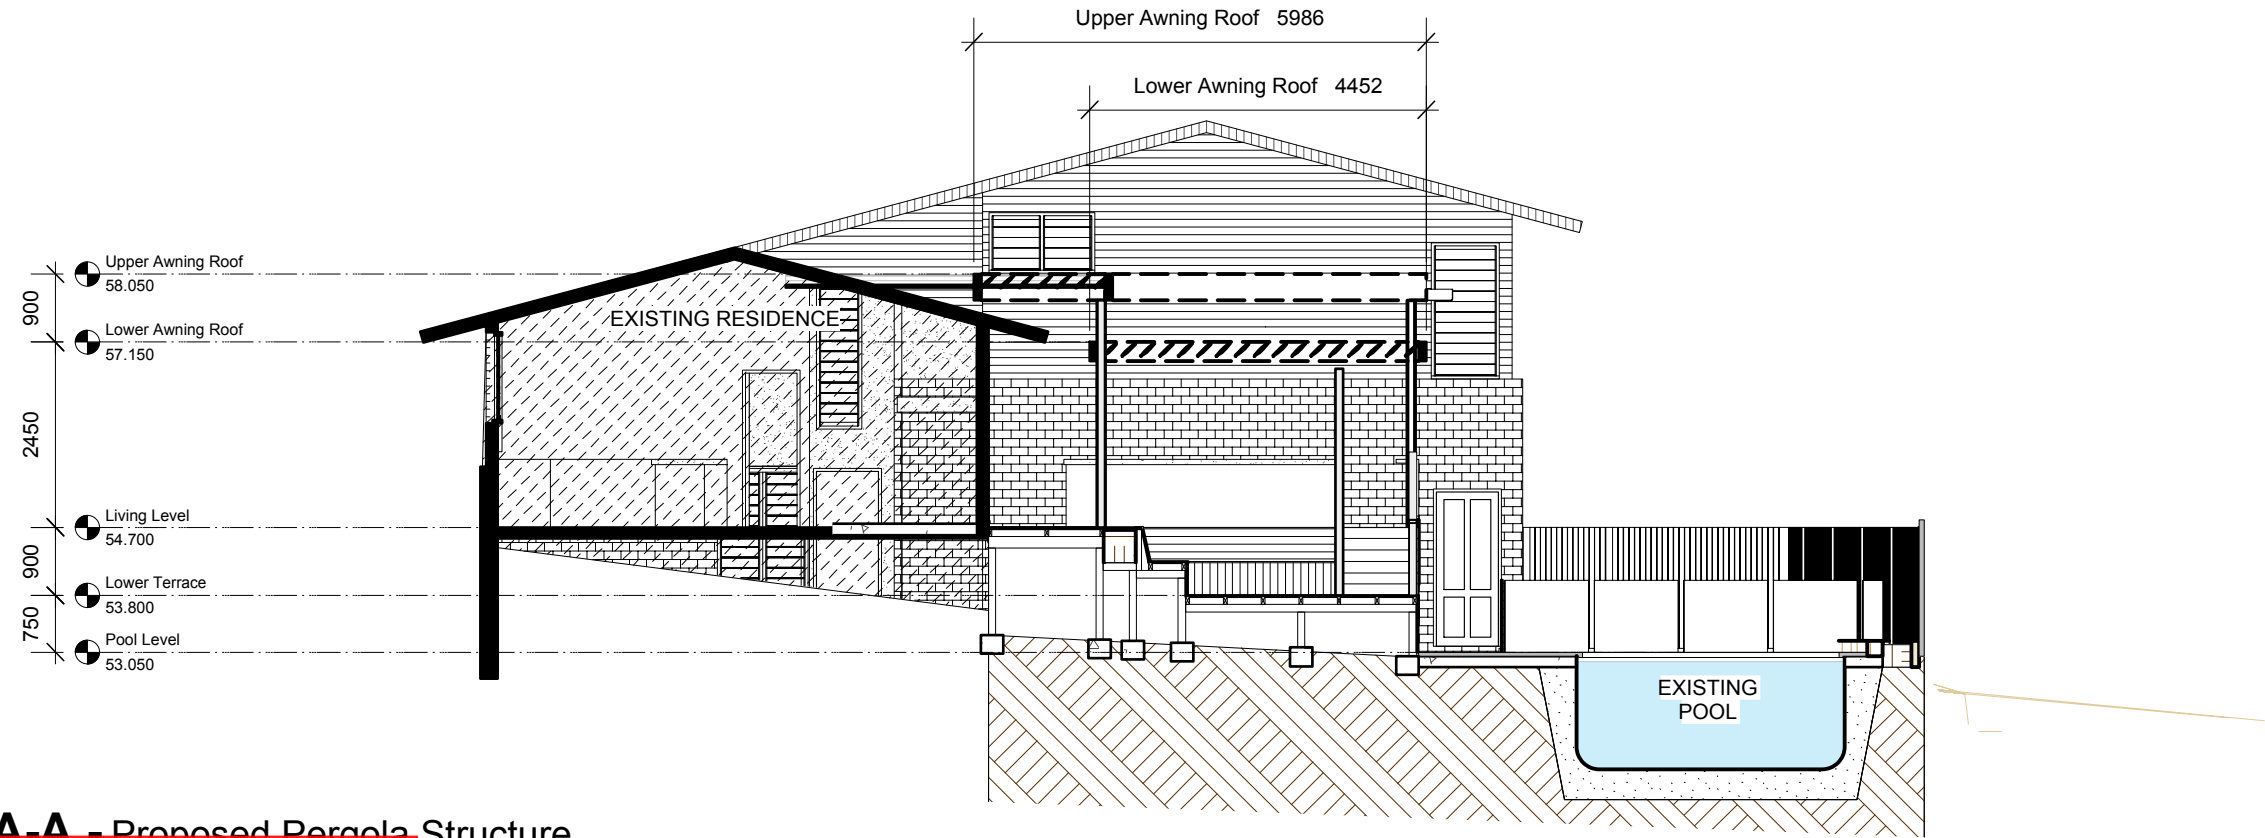

Section A-A - Proposed Pergola Structure



Scale 1:100

NEWCASTLE CITY COUNCIL

This plan / document is referred to in
Development Application No:
DA2019/00592

The application has been consented to subject to
compliance with conditions of consent.

Copyright: All documents have been reproduced by
Council for the purposes of complying with its statutory
obligations and may not be copied, used or otherwise
reproduced in whole or in part without the authority
of the copyright owner.

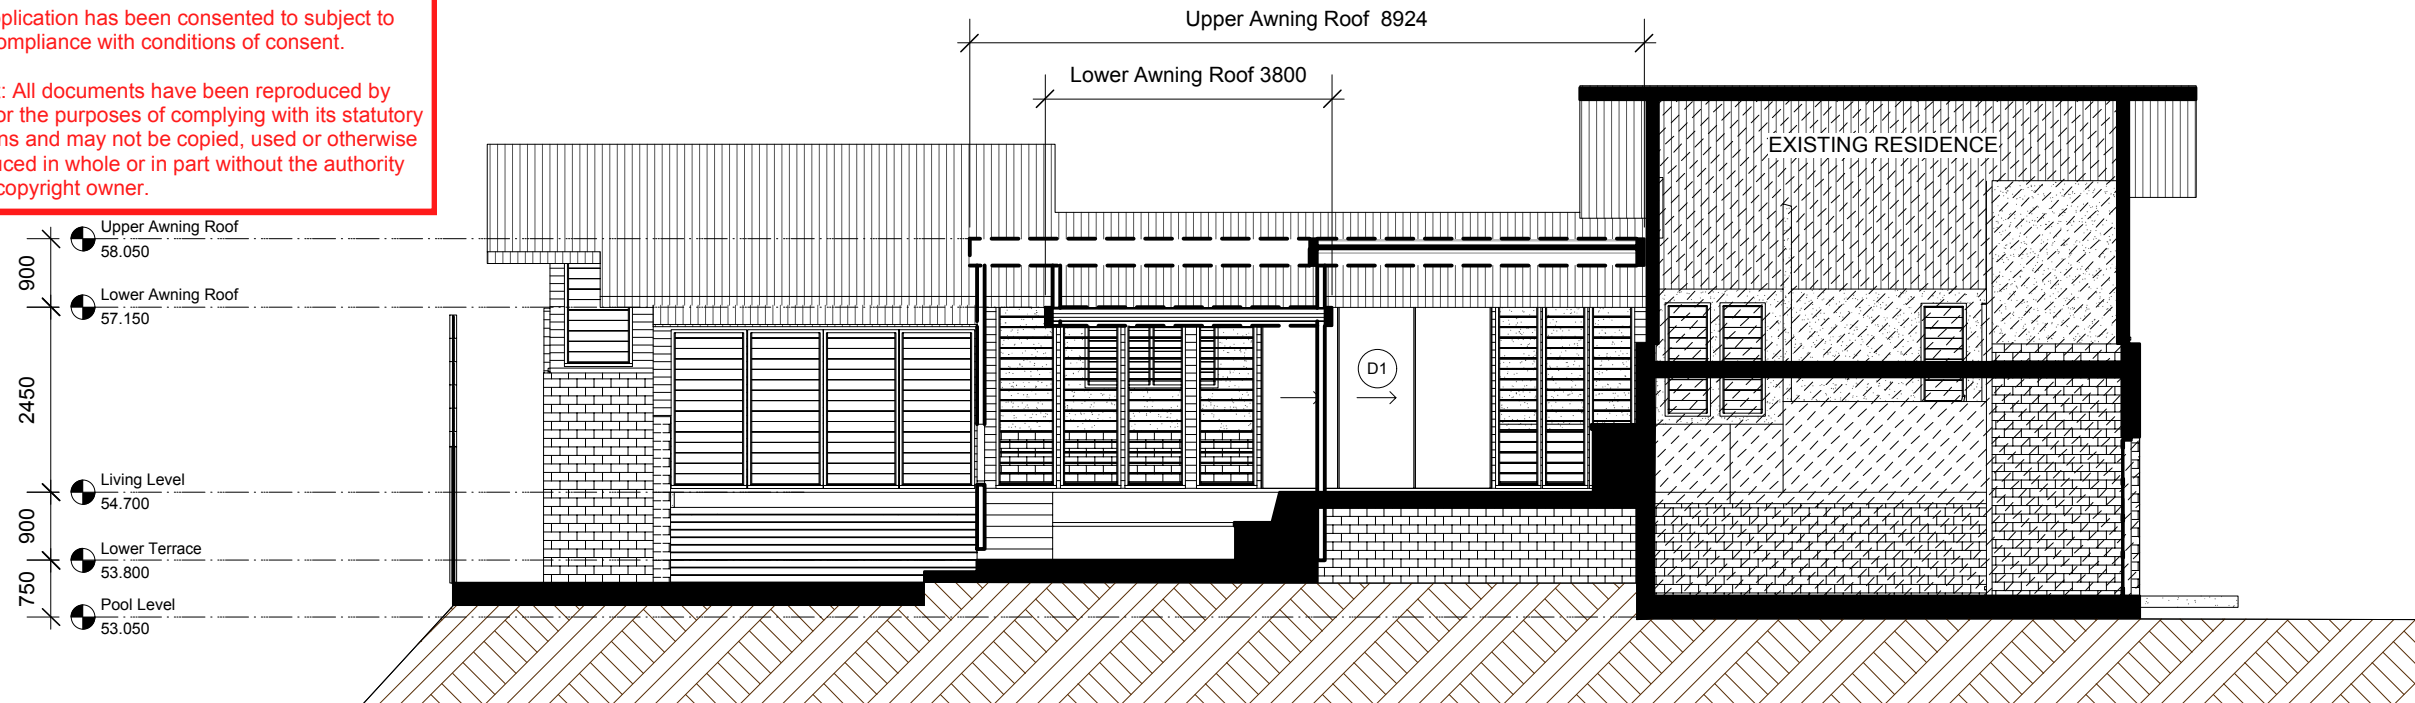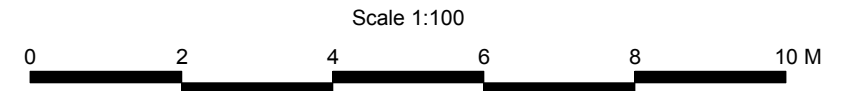

Section B-B - Proposed Pergola Structure

Scale 1:100

Landscape DA Documentation



DESIGN STUDIO
MUD LANDSCAPE DESIGN
The Roost, Level 1 152 - 158
Hunter Street, Newcastle, NSW, 2300

Phone 0415 883 167
Email hello@mud.design



A	15/11/18	1.0 Preliminary Landscape Concept Design	All	MT
B	11/12/18	2.0 Landscape Concept Design	All	MT
C	11/06/19	DA Documentation - Revision 1	All	MT
No.	Date	Revision Notes	Zone	By

Project Manager Mark Tisdell
Drawn By Mark Tisdell
Reviewed By Julia Jerome
Date 11/06/19
CAD File Name 1.0 4418WWitherdinCurzon.vwx

PROJECT ID:
0419WWitherdinCurzon

CLIENT:
Amber & David Witherdin

SITE:
47a Curzon Road
New Lambton, NSW, 2305

ISSUE:
Landscape DA Documentation

WORK TO FIGURED
DIMENSIONS IN
PREFERENCE TO SCALE.
CHECK DIMENSIONS AND
LEVELS ON SITE BEFORE
ORDERING MATERIALS OR
THE COMPLETION OF
WORKSHOP DRAWINGS

Drawing:

Sections

Print date:
11/06/19

Scale @ A3:
1:200

Page no.
2.06